
"CITY OF TKARONTO"

NOTE: THE NAME 'CITY OF TKARONTO' IS SYMBOLIC AND NOT GEOGRAPHICALLY TIED TO TORONTO. IT SERVES AS A TEACHING TOOL TO FAMILIARIZE STUDENTS WITH INDIGENOUS COMMUNITY NAMS AND CULTURAL CONTEXTS. RECOGNIZE THAT THIS FICTIONA; NAME REPRESENTS AN INDIGENOUS COMMUNITY AND NOT AN ACTUAL LOCATION

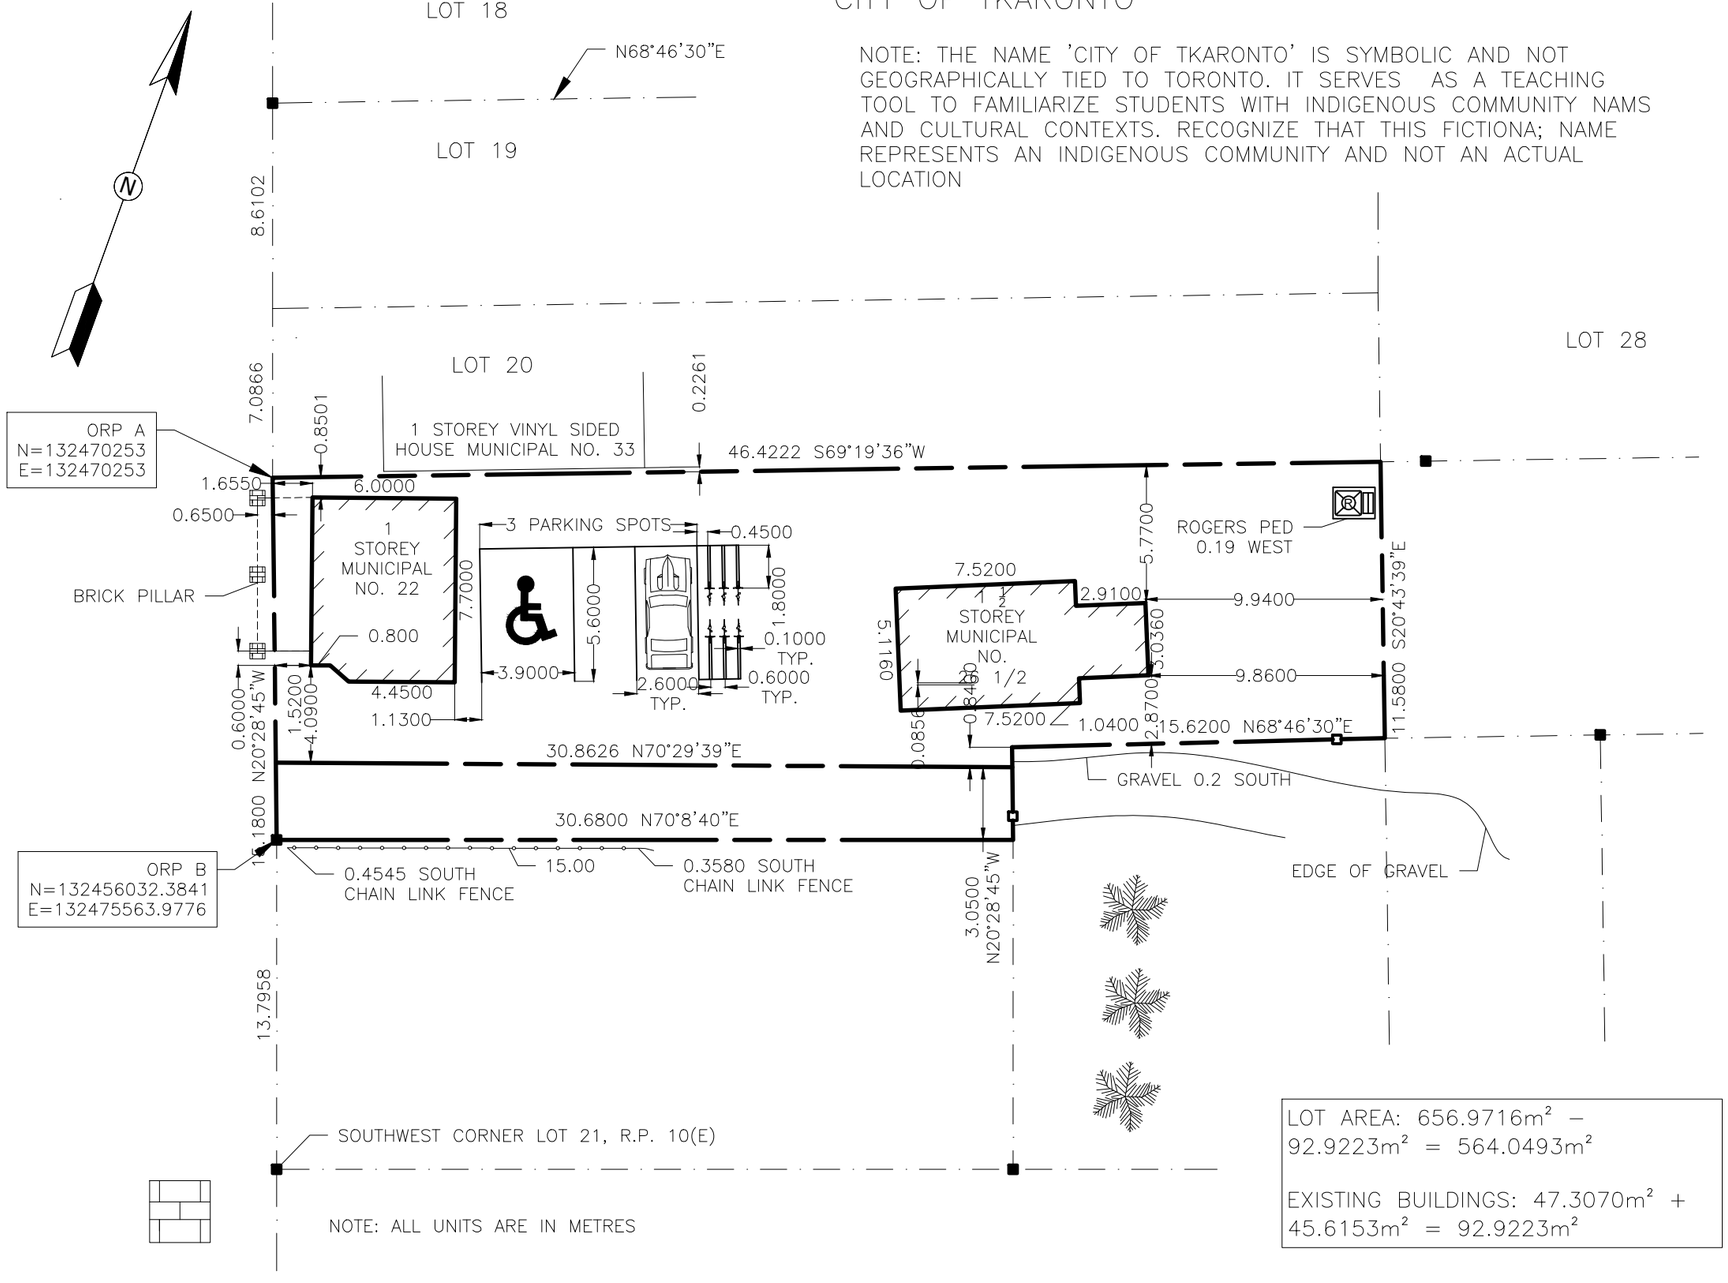

LOT AREA: 656.9716m² – 92.9223m² = 564.0493m²

EXISTING BUILDINGS: 47.3070m² + 45.6153m² = 92.9223m²

PLAN OF SURVEY

OF PART OF

LOT 21

REGISTERED PLAN NO. 10(E)

IN THE
CITY OF TKARONTO

4 2 0 4 8 12

1:250
(SCALE IN METRES)

LEGENDS:

UNLESS OTHERWISE NOTED ALL DIMENSIONS SHOWN ARE MEASURED

□	DENOTES SURVEY MONUMENT SET
■	DENOTES SURVEY MONUMENT FOUND
SIB	DENOTES STANDARD IRON BAR
IB	DENOTES IRON BAR
ORP	DENOTES OBSERVED REFERENCE POINT
N	DENOTES NORTH
W	DENOTES WEST
R.P.	DENOTES REGISTERED PLAN
PIN	DENOTES PARCEL IDENTIFICATION NUMBER
MUN	DENOTES MUNICIPAL NUMBER
No.	DENOTES NUMBER
ROW	DENOTES RIGHT–OF–WAY
NTS	NOT TO SCALE

NOTES:

- THIS DOCUMENT IS NOT A LEGAL PLAN AND SHOULD NOT BE USED FOR ANY OFFICIAL OR LEGAL URPOSES. IT IS PROVIDED EXCLUSIVELY FOR EDUCATIONAL EXERCISES, LEARNING EXPERIENCES, AND DRAFTING PRACTICE.

- THERE MAY BE ARCHAEOLOGICAL SITES, BURIAL GROUNDS, OR OTHER CULTURAL HERITAGE FEATURES OF IMPORTANCE TO THE LOCAL INDIGENOUS COMMUNITY IN PROXIMITY TO THE SURVEYED AREA. IT IS CRUCIAL TO RECOGNIZE AND PROTECT THESE SITES.

- THE INSTALLATION OF BIKE RACK ADJACENT TO THE DESIGNATED PARKING SPOTS DEMONSTRATE COMMITMENT TO PROMOTING SUSTAINABLE PRACTICES. THIS ENCOURAGES THE USE OF ALTERNATIVE TRANSPORTATION METHODS, CONTRIBUTING TO REDUCED ENVIRONMENTAL IMPACT AND IMPROVED OVERALL SUSTAINABILITY.

Drawing Title		Date	Submitted to:
PROPERTY PLAN		26/08/07	PROFESSOR MEHRNAZ
Drawn	Course Name	Scale	Sheet
OKAFOR CHRISTIAN IZUNNA	BEA101NZZ	1:250	C1